



| REV. | CHANGE DETAILS | DATE | PREPARED | APPD. |
|------|----------------|------|----------|-------|
| 13   |                |      |          |       |
| 14   |                |      |          |       |
| 15   |                |      |          |       |
| 16   |                |      |          |       |

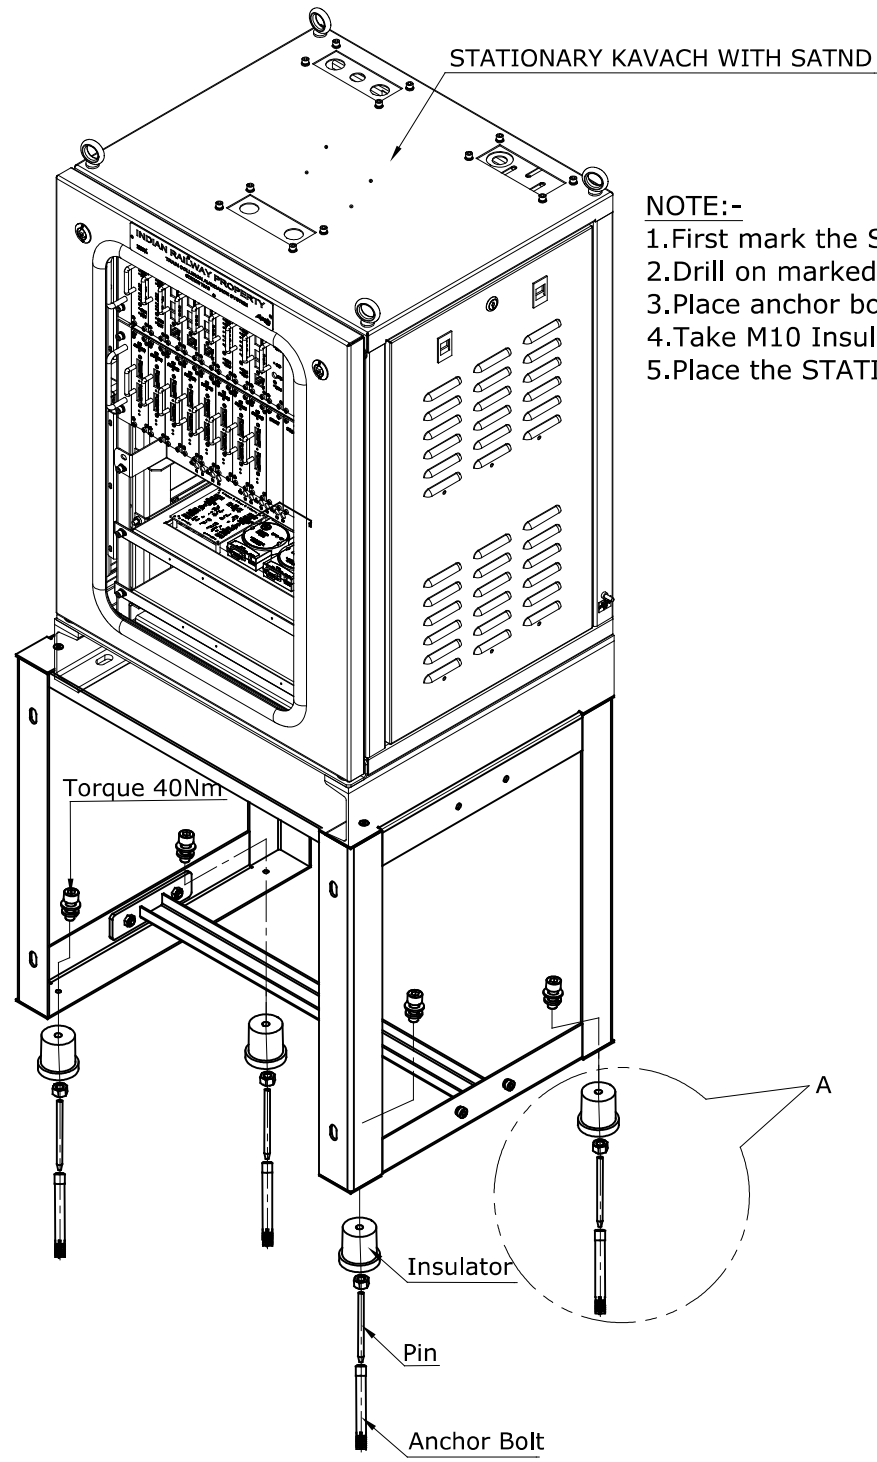

**NOTE:-**

- 1.First mark the STATIONARY KAVACH on floor / ground as per STD Kavach Floor Plan
- 2.Drill on marked position to seat M10 Anchor bolt pin type
- 3.Place anchor bolt into drilled hole & insert pin assembly.
- 4.Take M10 Insulator & fix it in anchor bolt & tightend to torque of 40Nm.
- 5.Place the STATIONARY KAVACH on fixed insulator & tighned by M10 bolts to torque of 40Nm

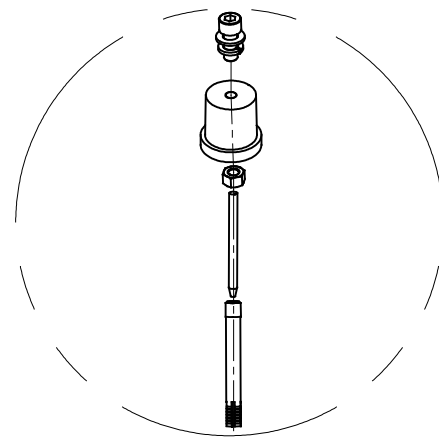

View - A  
Details Anchor Bolt assembly  
Enlarged View

|                                |                      |   |                                  |             |
|--------------------------------|----------------------|---|----------------------------------|-------------|
| PROJECT:<br>KAVACH             | HBL Engineering Ltd. | NAME<br>P. SHIVA KUMAR   | DESIGNATION<br>Sr. ENGINEER      | SIGN.       |
| ASSEMBLY:<br>STATIONARY KAVACH |                      | CHECKED<br>CH. SHIVA GANESH   | Sp. ENGINEER                     |             |
|                                |                      | APPROVED<br>Y. SUBRAMANYAM   | GENERAL MANAGER<br>(ENGINEERING) |             |
| SCALE:<br>NTS                  | SIZE:<br>A1          | TITLE:<br>Stationary_Kavach_Installation_Drawing   | DRAWING NO.<br>5 18 76 0056      | REV.<br>1.0 |
|                                |                      |   | PART NO.                         |             |
| EFFECTIVE FROM:                |                      | TOLERANCE NOT SPECIFIED SHALL BE AS PER IS : 2102 - 1993.   |                                  |             |
| ALL DIMENSIONS ARE IN mm       |                      | THIS DRAWING IS THE PROPERTY OF HBL ENGINEERING LIMITED AND MUST NOT BE COPIED, REPRODUCED, TRANSMITTED OR DISCLOSED TO ANY THIRD PARTY WITHOUT THE WRITTEN CONSENT OF THE COMPANY. |                                  |             |



# 516760056\_Stationary\_Kavach\_Installation\_Drawing

Final Audit Report

2026-03-30

|                 |                                                |
|-----------------|------------------------------------------------|
| Created:        | 2026-03-27 (India Standard Time)               |
| By:             | Subrahmanyam Y (subrahmanyam.yadavalli@hbl.in) |
| Status:         | Signed                                         |
| Transaction ID: | CBJCHBCAABAAAN90yCdvfBH3sAFaN4sV4yqxN1cWGZaP4  |

## "516760056\_Stationary\_Kavach\_Installation\_Drawing" History

-  Document created by Subrahmanyam Y (subrahmanyam.yadavalli@hbl.in)  
2026-03-27 - 4:21:34 PM GMT+5.5- IP address: 122.187.81.114
-  Document emailed to P Shiva Kumar (shivakumar.pudhoju@hbl.in) for signature  
2026-03-27 - 4:22:57 PM GMT+5.5
-  Email viewed by P Shiva Kumar (shivakumar.pudhoju@hbl.in)  
2026-03-27 - 4:25:43 PM GMT+5.5- IP address: 122.187.81.114
-  Document e-signed by P Shiva Kumar (shivakumar.pudhoju@hbl.in)  
Signature Date: 2026-03-27 - 4:26:48 PM GMT+5.5 - Time Source: server- IP address: 122.187.81.114
-  Document emailed to sivajiganesh.chennuboyina@hbl.in for signature  
2026-03-27 - 4:26:50 PM GMT+5.5
-  Email viewed by sivajiganesh.chennuboyina@hbl.in  
2026-03-27 - 4:28:10 PM GMT+5.5- IP address: 122.187.81.114
-  Signer sivajiganesh.chennuboyina@hbl.in entered name at signing as CH.Slvajiganesh  
2026-03-27 - 4:29:07 PM GMT+5.5- IP address: 122.187.81.114
-  Document e-signed by CH.Slvajiganesh (sivajiganesh.chennuboyina@hbl.in)  
Signature Date: 2026-03-27 - 4:29:09 PM GMT+5.5 - Time Source: server- IP address: 122.187.81.114
-  Document emailed to Subrahmanyam Y (subrahmanyam.yadavalli@hbl.in) for signature  
2026-03-27 - 4:29:11 PM GMT+5.5
-  Email viewed by Subrahmanyam Y (subrahmanyam.yadavalli@hbl.in)  
2026-03-30 - 9:08:44 AM GMT+5.5- IP address: 122.187.81.114



Document e-signed by Subrahmanyam Y (subrahmanyam.yadavalli@hbl.in)

Signature Date: 2026-03-30 - 9:09:07 AM GMT+5.5 - Time Source: server- IP address: 122.187.81.114



Agreement completed.

2026-03-30 - 9:09:07 AM GMT+5.5