


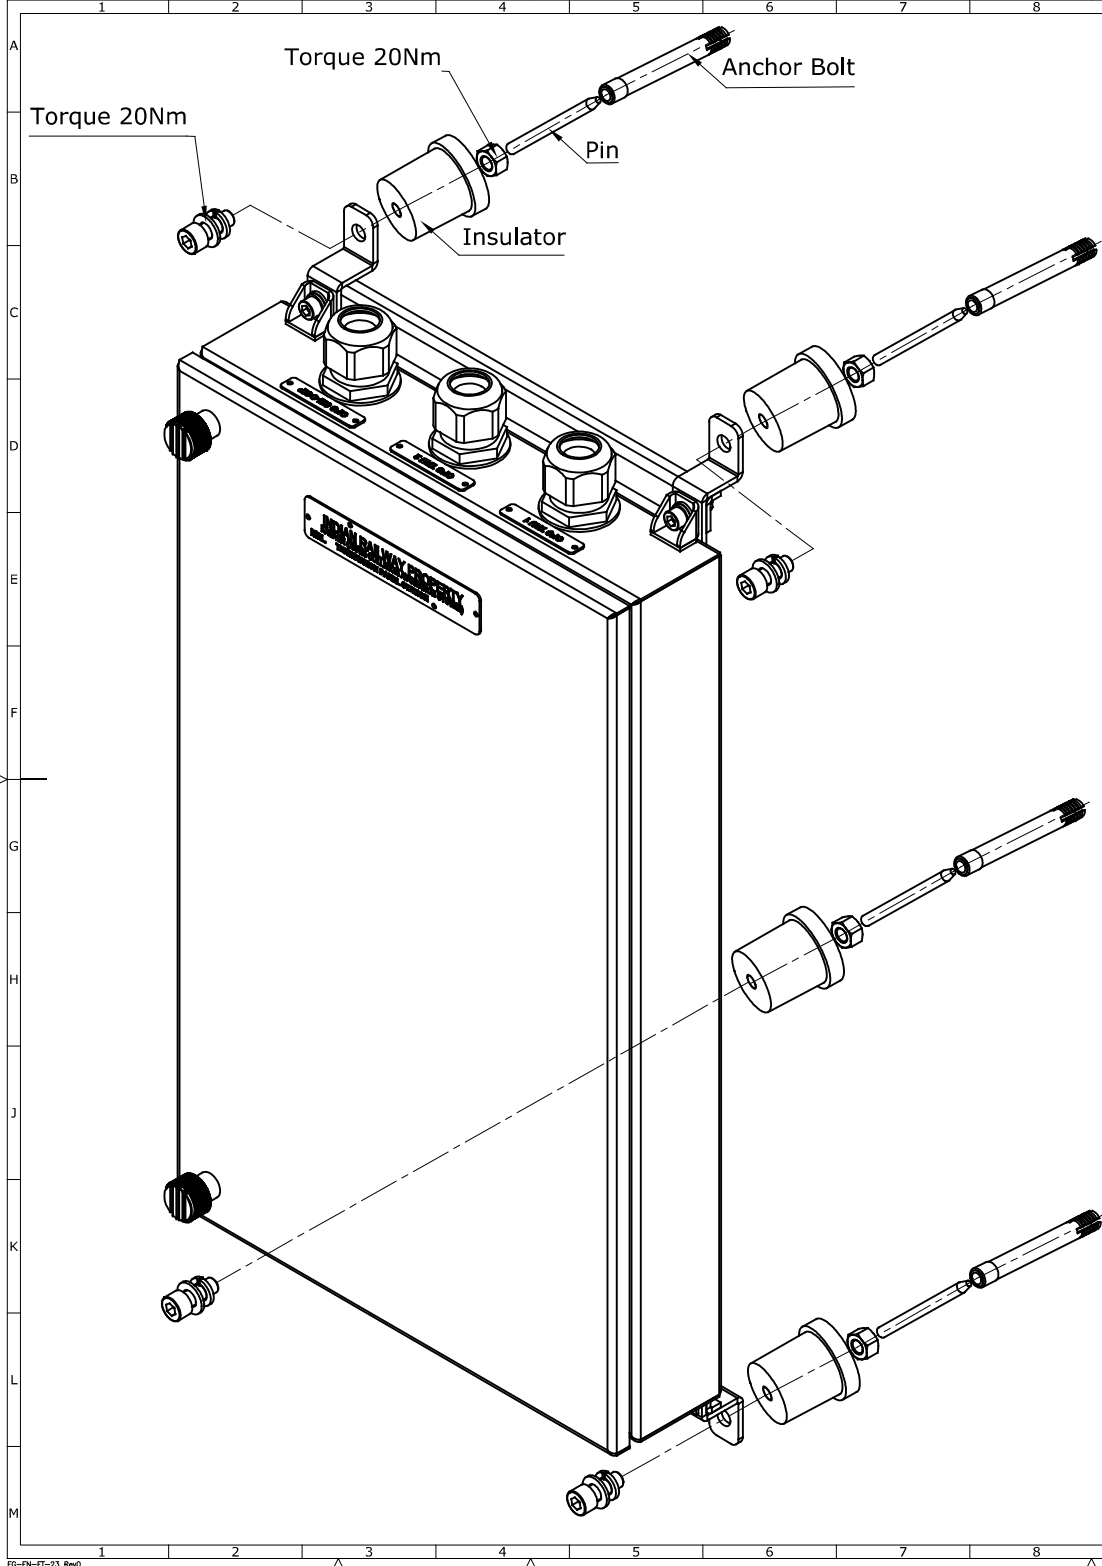

NOTE:-

- 1.First mark the Station termination panel on wall as per STD Kavach Floor Plan
- 2.Drill on marks position to seat M8 Anchor bolt pin type
- 3.Place anchor bolt into drilled hole & insert pin assembly.
- 4.Take M8 Insulator & fix it in anchor bolt & tightend to torque of 20Nm.
- 5.Place the Station termination panel on fixed insulator & tighned by M8 bolts to torque of 20Nm

REV.	CHANGE DETAILS	DATE	PREPARED	APPD.
13				
14				
15				
16				

PROJECT: KAVACH	NAME P. SHIVA KUMAR	DESIGNATION Sr. ENGINEER	SIGN.
ASSEMBLY: STATIONARY KAVACH	CHECKED CH. SHIVA GANESH	Sp. ENGINEER	
	APPROVED Y. SUBRAMANYAM	GENERAL MANAGER (ENGINEERING)	
SCALE: NTS	SHEET: 1 OF 1	TITLE: KAVACH_STATIONARY_TERMINATION_PANEL INSTALLATION_DRAWING	DRAWING NO. 5 16 76 0045 PART NO.
EFFECTIVE FROM:		TOLERANCE NOT SPECIFIED SHALL BE AS PER IS : 2102 - 1993.	
ALL DIMENSIONS ARE IN mm		THIS DRAWING IS THE PROPERTY OF HBL ENGINEERING LIMITED AND MUST NOT BE COPIED, REPRODUCED, TRANSMITTED OR DISCLOSED TO ANY THIRD PARTY WITHOUT THE WRITTEN CONSENT OF THE COMPANY.	

516760045_KAVACH_STATIONARY_TERMINATION_PANEL_INSTALLATION_DRAWING

Final Audit Report

2026-03-30

Created:	2026-03-27 (India Standard Time)
By:	Subrahmanyam Y (subrahmanyam.yadavalli@hbl.in)
Status:	Signed
Transaction ID:	CBJCHBCAABAAiCLJFxx_EQS1-OZKPc8zoA7auZC8-KoY

"516760045_KAVACH_STATIONARY_TERMINATION_PANEL_INSTALLATION_DRAWING" History

-  Document created by Subrahmanyam Y (subrahmanyam.yadavalli@hbl.in)
2026-03-27 - 2:20:53 PM GMT+5.5- IP address: 122.187.81.114
-  Document emailed to P Shiva Kumar (shivakumar.pudhoju@hbl.in) for signature
2026-03-27 - 2:23:28 PM GMT+5.5
-  Email viewed by P Shiva Kumar (shivakumar.pudhoju@hbl.in)
2026-03-27 - 2:28:28 PM GMT+5.5- IP address: 122.187.81.114
-  Document e-signed by P Shiva Kumar (shivakumar.pudhoju@hbl.in)
Signature Date: 2026-03-27 - 2:28:51 PM GMT+5.5 - Time Source: server- IP address: 122.187.81.114
-  Document emailed to sivajiganesh.chennuboyina@hbl.in for signature
2026-03-27 - 2:28:52 PM GMT+5.5
-  Email viewed by sivajiganesh.chennuboyina@hbl.in
2026-03-27 - 2:55:20 PM GMT+5.5- IP address: 122.187.81.114
-  Signer sivajiganesh.chennuboyina@hbl.in entered name at signing as CH.Sivajiganesh
2026-03-27 - 2:58:28 PM GMT+5.5- IP address: 122.187.81.114
-  Document e-signed by CH.Sivajiganesh (sivajiganesh.chennuboyina@hbl.in)
Signature Date: 2026-03-27 - 2:58:30 PM GMT+5.5 - Time Source: server- IP address: 122.187.81.114
-  Document emailed to Subrahmanyam Y (subrahmanyam.yadavalli@hbl.in) for signature
2026-03-27 - 2:58:31 PM GMT+5.5
-  Email viewed by Subrahmanyam Y (subrahmanyam.yadavalli@hbl.in)
2026-03-30 - 9:14:09 AM GMT+5.5- IP address: 122.187.81.114



Document e-signed by Subrahmanyam Y (subrahmanyam.yadavalli@hbl.in)

Signature Date: 2026-03-30 - 9:14:36 AM GMT+5.5 - Time Source: server- IP address: 122.187.81.114



Agreement completed.

2026-03-30 - 9:14:36 AM GMT+5.5