
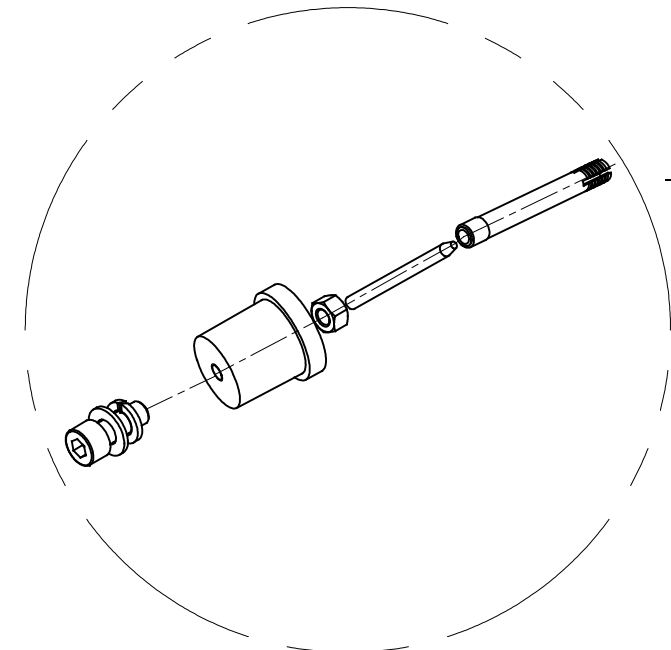


REV.	CHANGE DETAILS	DATE	PREPARED	APPD.
13				
14				
15				
16				

NOTE:-

- 1.First mark the SM OCIP termination panel on wall as per STD Kavach Floor Plan
- 2.Drill on marks position to seat M8 Anchor bolt pin type
- 3.Place anchor bolt into drilled hole & insert pin assembly.
- 4.Take M8 Insulator & fix it in anchor bolt & tightend to torque of 20Nm.
- 5.Place SM OCIP termination panel & fix it by M6 screws apply torque of 8Nm.

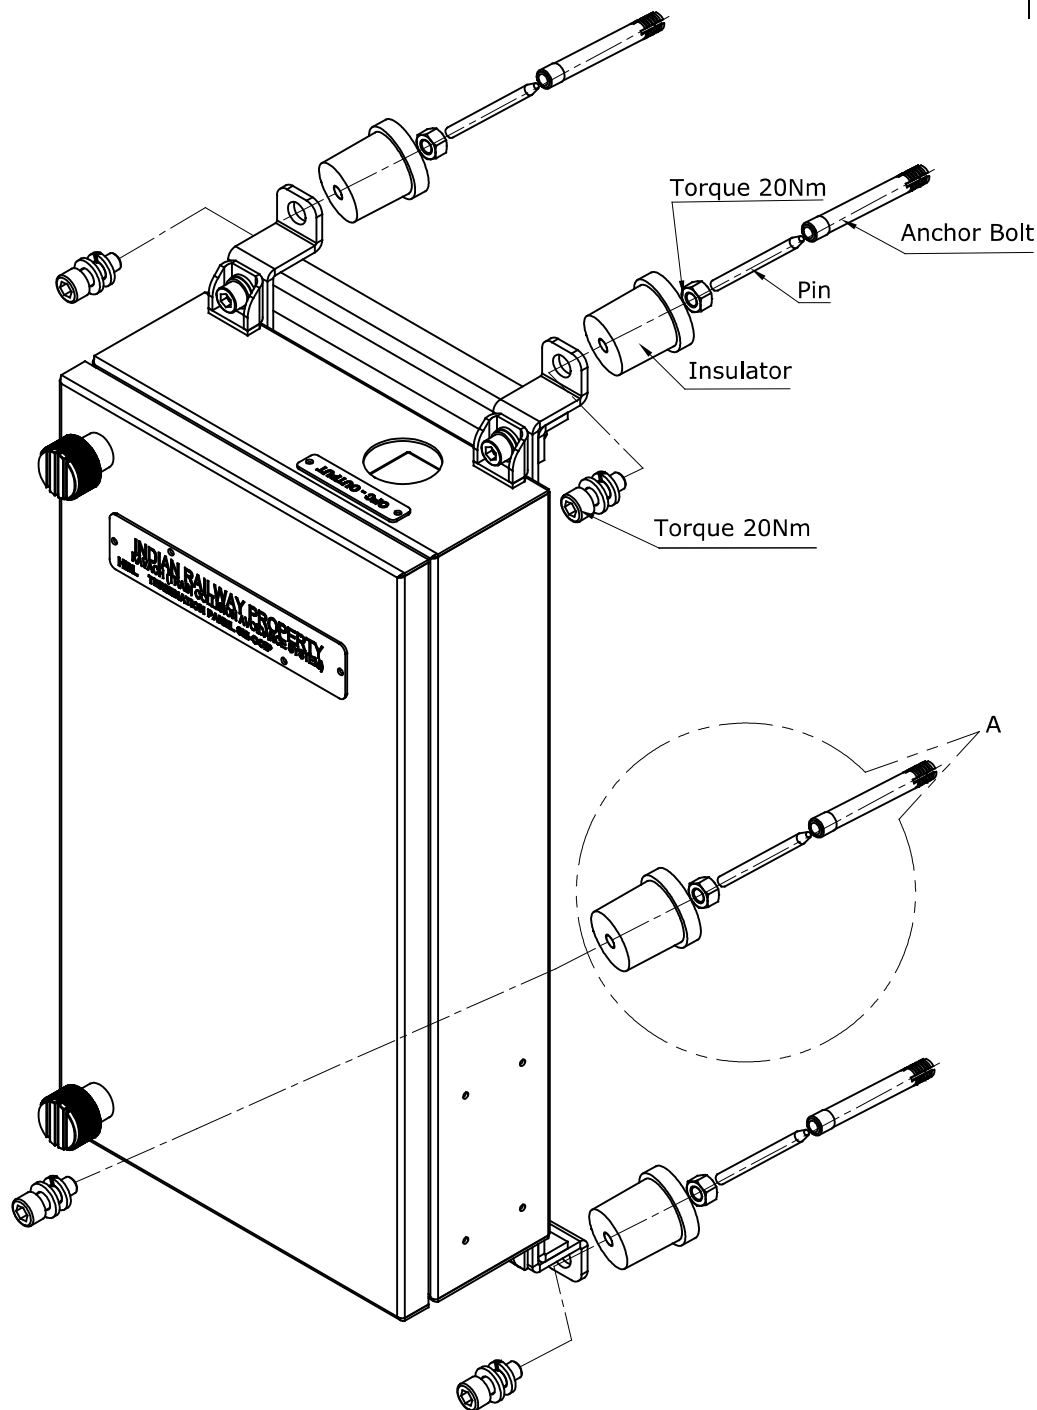

View - A
Details Anchor Bolt assembly
Enlarged View

PROJECT: KAVACH				NAME		DESIGNATION		SIGN.	
ASSEMBLY: STATIONARY KAVACH		HBL Engineering Ltd.		DESIGN		P. SHIVA KUMAR		SR. ENGINEER	
CHECKED:				CHECKED		CH. SHIVA GANESH		SR. ENGINEER	
APPROVED:				APPROVED:		Y. SUBRAMANYAM		GENERAL MANAGER (ENGINEERING)	
SCALE:		SIZE:		TITLE:		DRAWING NO.		5 16 76 0046	
NTS		A1		KAVACH_SM_OCIP_TERMINATION_PANEL		PART NO.		REV. 1.0	
SHEET:		1 OF 1		INSTALLATION_DRAWING					
EFFECTIVE FROM:		ALL DIMENSIONS ARE IN mm		TOLERANCE NOT SPECIFIED SHALL BE AS PER IS : 2102 - 1993.		THIS DRAWING IS THE PROPERTY OF HBL ENGINEERING LIMITED AND MUST NOT BE COPIED, REPRODUCED, TRANSMITTED OR DISCLOSED TO ANY THIRD PARTY WITHOUT THE WRITTEN CONSENT OF THE COMPANY.			

516760046_KAVACH_SM OCIP_TERMINATION_PANEL_INSTALLATION_DRAWING

Final Audit Report

2026-03-30

Created:	2026-03-27 (India Standard Time)
By:	Subrahmanyam Y (subrahmanyam.yadavalli@hbl.in)
Status:	Signed
Transaction ID:	CBJCHBCAABAAPtViKe1T9GNRBLZj9aA13azz_QpPgVg

"516760046_KAVACH_SM OCIP_TERMINATION_PANEL_INSTALLATION_DRAWING" History

-  Document created by Subrahmanyam Y (subrahmanyam.yadavalli@hbl.in)
2026-03-27 - 2:24:15 PM GMT+5.5- IP address: 122.187.81.114
-  Document emailed to P Shiva Kumar (shivakumar.pudhoju@hbl.in) for signature
2026-03-27 - 2:26:04 PM GMT+5.5
-  Email viewed by P Shiva Kumar (shivakumar.pudhoju@hbl.in)
2026-03-27 - 2:28:58 PM GMT+5.5- IP address: 122.187.81.114
-  Document e-signed by P Shiva Kumar (shivakumar.pudhoju@hbl.in)
Signature Date: 2026-03-27 - 2:29:22 PM GMT+5.5 - Time Source: server- IP address: 122.187.81.114
-  Document emailed to sivajiganesh.chennuboyina@hbl.in for signature
2026-03-27 - 2:29:24 PM GMT+5.5
-  Email viewed by sivajiganesh.chennuboyina@hbl.in
2026-03-27 - 2:59:09 PM GMT+5.5- IP address: 122.187.81.114
-  Signer sivajiganesh.chennuboyina@hbl.in entered name at signing as CH.Sivajiganesh
2026-03-27 - 3:00:44 PM GMT+5.5- IP address: 122.187.81.114
-  Document e-signed by CH.Sivajiganesh (sivajiganesh.chennuboyina@hbl.in)
Signature Date: 2026-03-27 - 3:00:46 PM GMT+5.5 - Time Source: server- IP address: 122.187.81.114
-  Document emailed to Subrahmanyam Y (subrahmanyam.yadavalli@hbl.in) for signature
2026-03-27 - 3:00:48 PM GMT+5.5
-  Email viewed by Subrahmanyam Y (subrahmanyam.yadavalli@hbl.in)
2026-03-30 - 9:13:14 AM GMT+5.5- IP address: 122.187.81.114



Document e-signed by Subrahmanyam Y (subrahmanyam.yadavalli@hbl.in)

Signature Date: 2026-03-30 - 9:13:51 AM GMT+5.5 - Time Source: server- IP address: 122.187.81.114



Agreement completed.

2026-03-30 - 9:13:51 AM GMT+5.5