


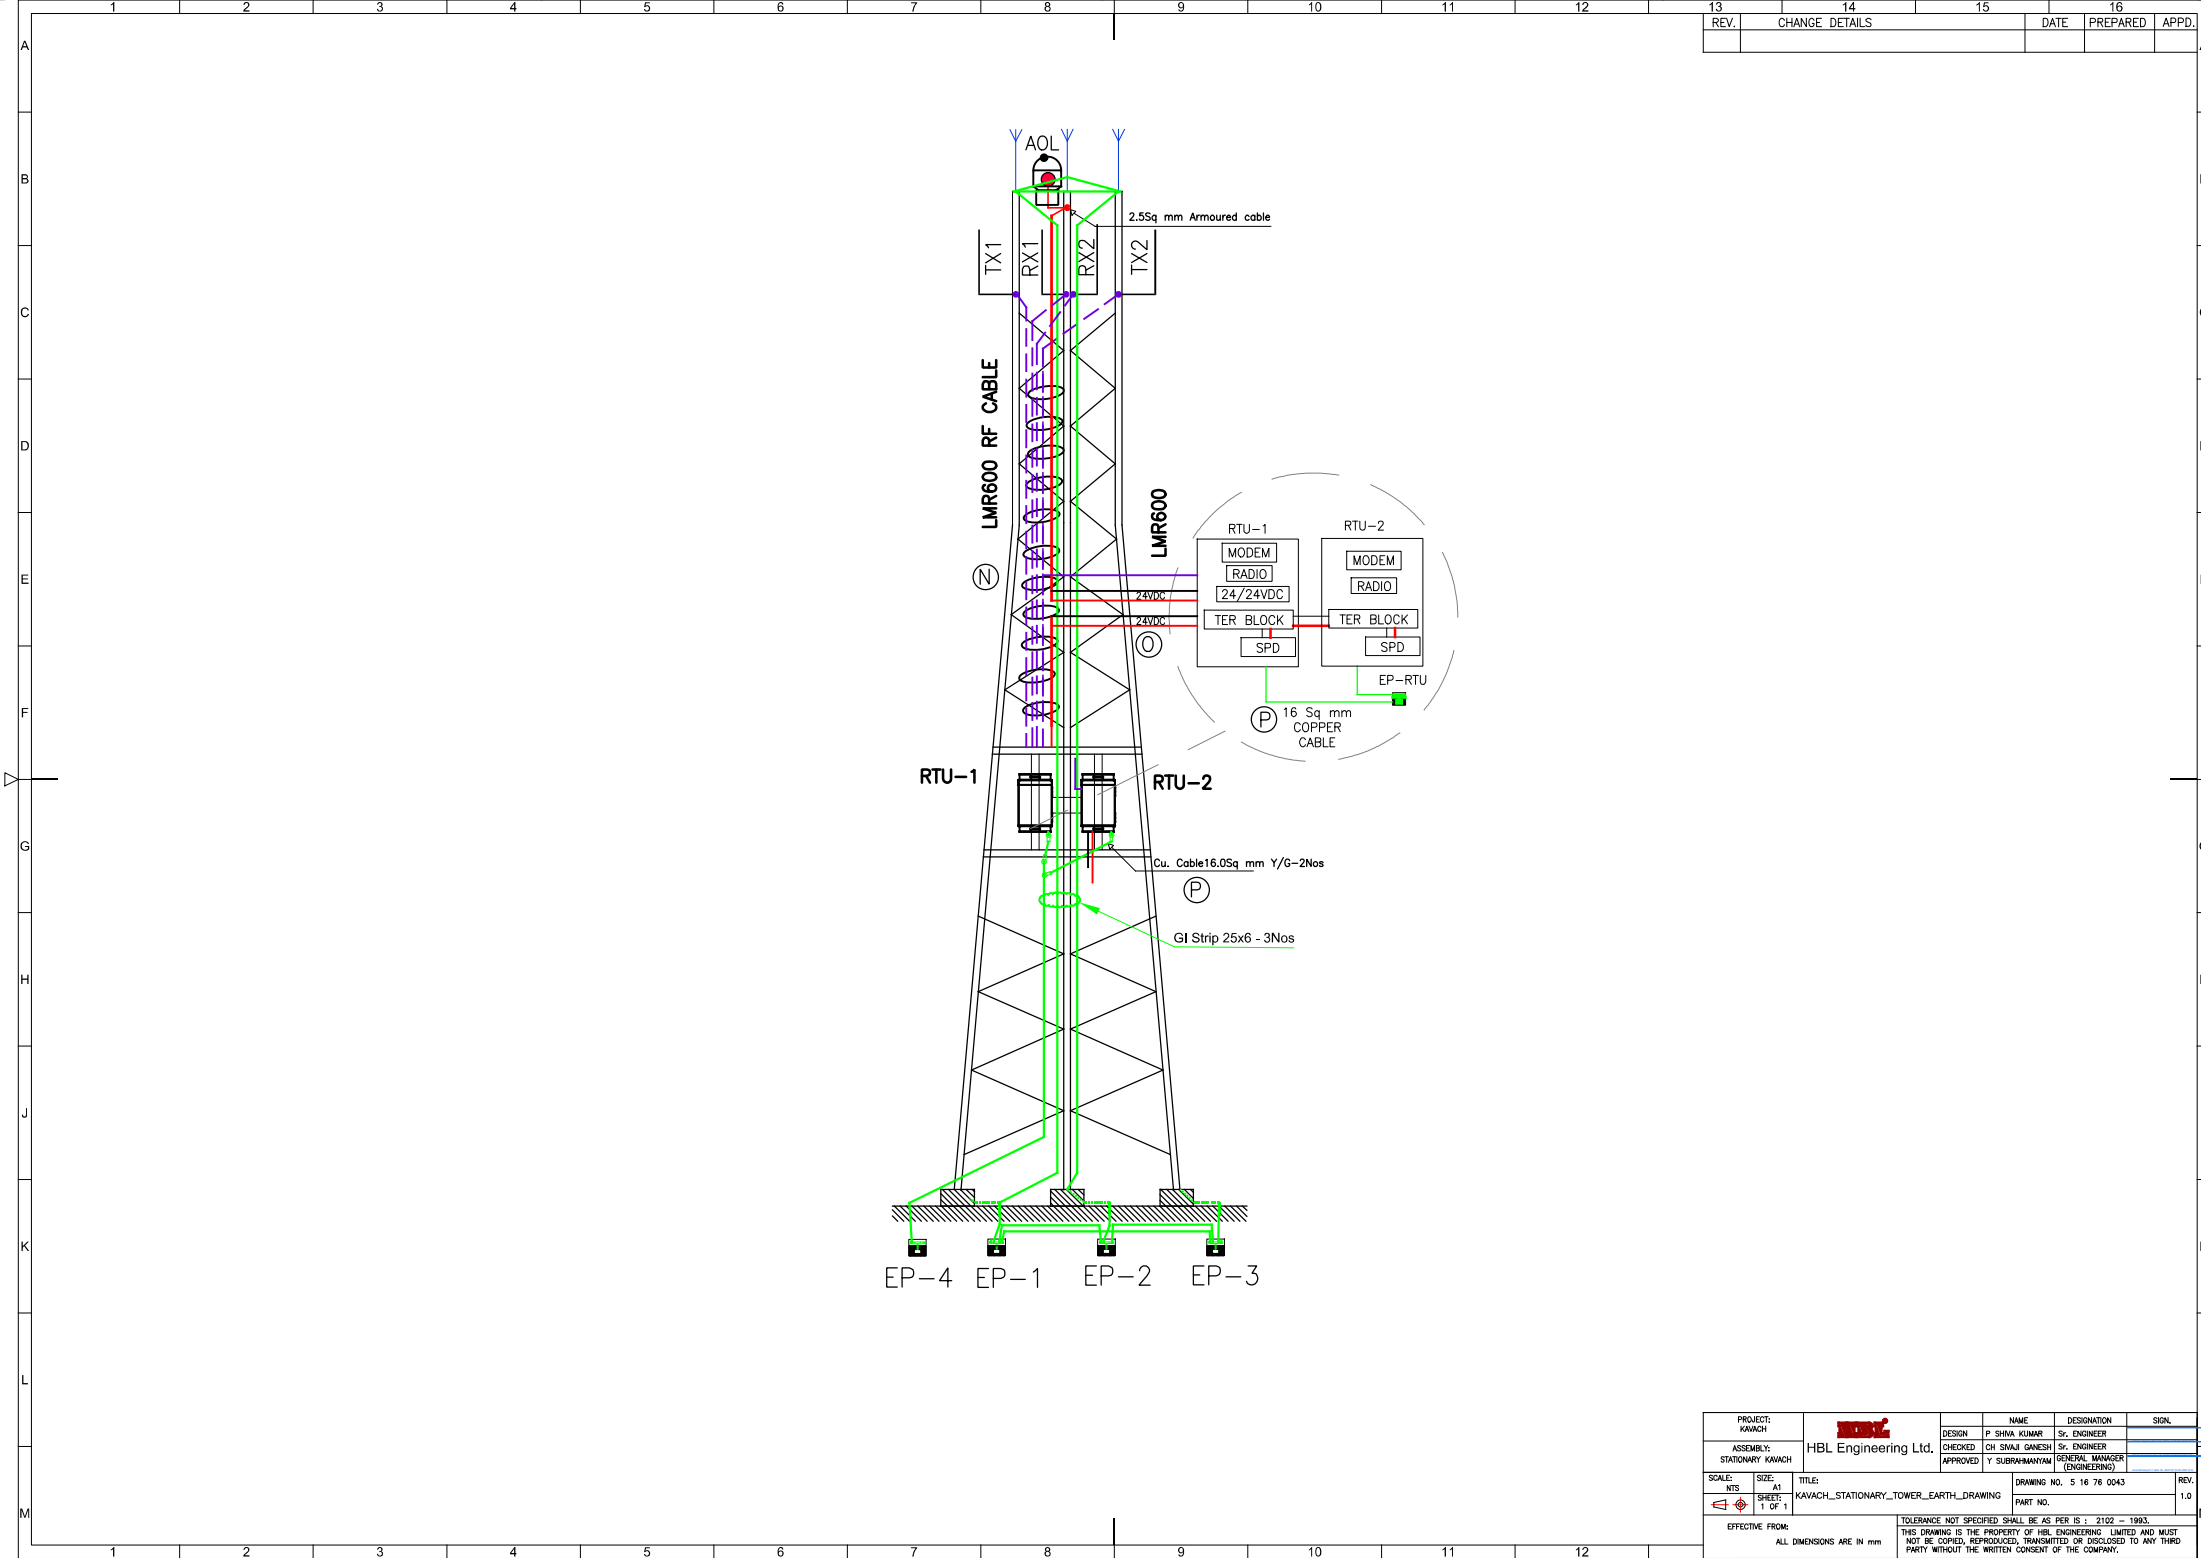

PROJECT: KAVACH		NAME		DESIGNATION	SIGN.
ASSEMBLY: STATIONARY KAVACH		HBL Engineering Ltd.		DESIGN	P. SHIVA KUMAR Sr. ENGINEER
SCALE: NTS		SIZE: A1		CHECKED	CH. SHIVA GANESH Sr. ENGINEER
SHEETS: 1 OF 1		TITLE: KAVACH_STATIONARY_TOWER_EARTH_DRAWING		APPROVED	Y. SUBRAMANYAM GENERAL MANAGER (ENGINEERING)
EFFECTIVE FROM:		TOLERANCE NOT SPECIFIED SHALL BE AS PER IS : 2102 - 1993.		DRAWING NO. 5 16 76 0043	
ALL DIMENSIONS ARE IN mm		THIS DRAWING IS THE PROPERTY OF HBL ENGINEERING LIMITED AND MUST NOT BE COPIED, REPRODUCED, TRANSMITTED OR DISCLOSED TO ANY THIRD PARTY WITHOUT THE WRITTEN CONSENT OF THE COMPANY.		PART NO.	

516760043_KAVACH_STATIONARY_TOWER_EARTH_DRAWING

Final Audit Report

2026-03-30

Created:	2026-03-27 (India Standard Time)
By:	Subrahmanyam Y (subrahmanyam.yadavalli@hbl.in)
Status:	Signed
Transaction ID:	CBJCHBCAABAAh4utfNHYRmfh_NTY6uUDK86hz95bcUZD

"516760043_KAVACH_STATIONARY_TOWER_EARTH_DRAWING" History

-  Document created by Subrahmanyam Y (subrahmanyam.yadavalli@hbl.in)
2026-03-27 - 2:18:14 PM GMT+5.5- IP address: 122.187.81.114
-  Document emailed to P Shiva Kumar (shivakumar.pudhoju@hbl.in) for signature
2026-03-27 - 2:20:17 PM GMT+5.5
-  Email viewed by P Shiva Kumar (shivakumar.pudhoju@hbl.in)
2026-03-27 - 2:27:24 PM GMT+5.5- IP address: 122.187.81.114
-  Document e-signed by P Shiva Kumar (shivakumar.pudhoju@hbl.in)
Signature Date: 2026-03-27 - 2:28:23 PM GMT+5.5 - Time Source: server- IP address: 122.187.81.114
-  Document emailed to sivajiganesh.chennuboyina@hbl.in for signature
2026-03-27 - 2:28:24 PM GMT+5.5
-  Email viewed by sivajiganesh.chennuboyina@hbl.in
2026-03-27 - 2:46:58 PM GMT+5.5- IP address: 122.187.81.114
-  Signer sivajiganesh.chennuboyina@hbl.in entered name at signing as CH.Sivajiganesh
2026-03-27 - 2:55:14 PM GMT+5.5- IP address: 122.187.81.114
-  Document e-signed by CH.Sivajiganesh (sivajiganesh.chennuboyina@hbl.in)
Signature Date: 2026-03-27 - 2:55:16 PM GMT+5.5 - Time Source: server- IP address: 122.187.81.114
-  Document emailed to Subrahmanyam Y (subrahmanyam.yadavalli@hbl.in) for signature
2026-03-27 - 2:55:18 PM GMT+5.5
-  Email viewed by Subrahmanyam Y (subrahmanyam.yadavalli@hbl.in)
2026-03-30 - 9:14:51 AM GMT+5.5- IP address: 122.187.81.114



Document e-signed by Subrahmanyam Y (subrahmanyam.yadavalli@hbl.in)

Signature Date: 2026-03-30 - 9:15:29 AM GMT+5.5 - Time Source: server- IP address: 122.187.81.114



Agreement completed.

2026-03-30 - 9:15:29 AM GMT+5.5