



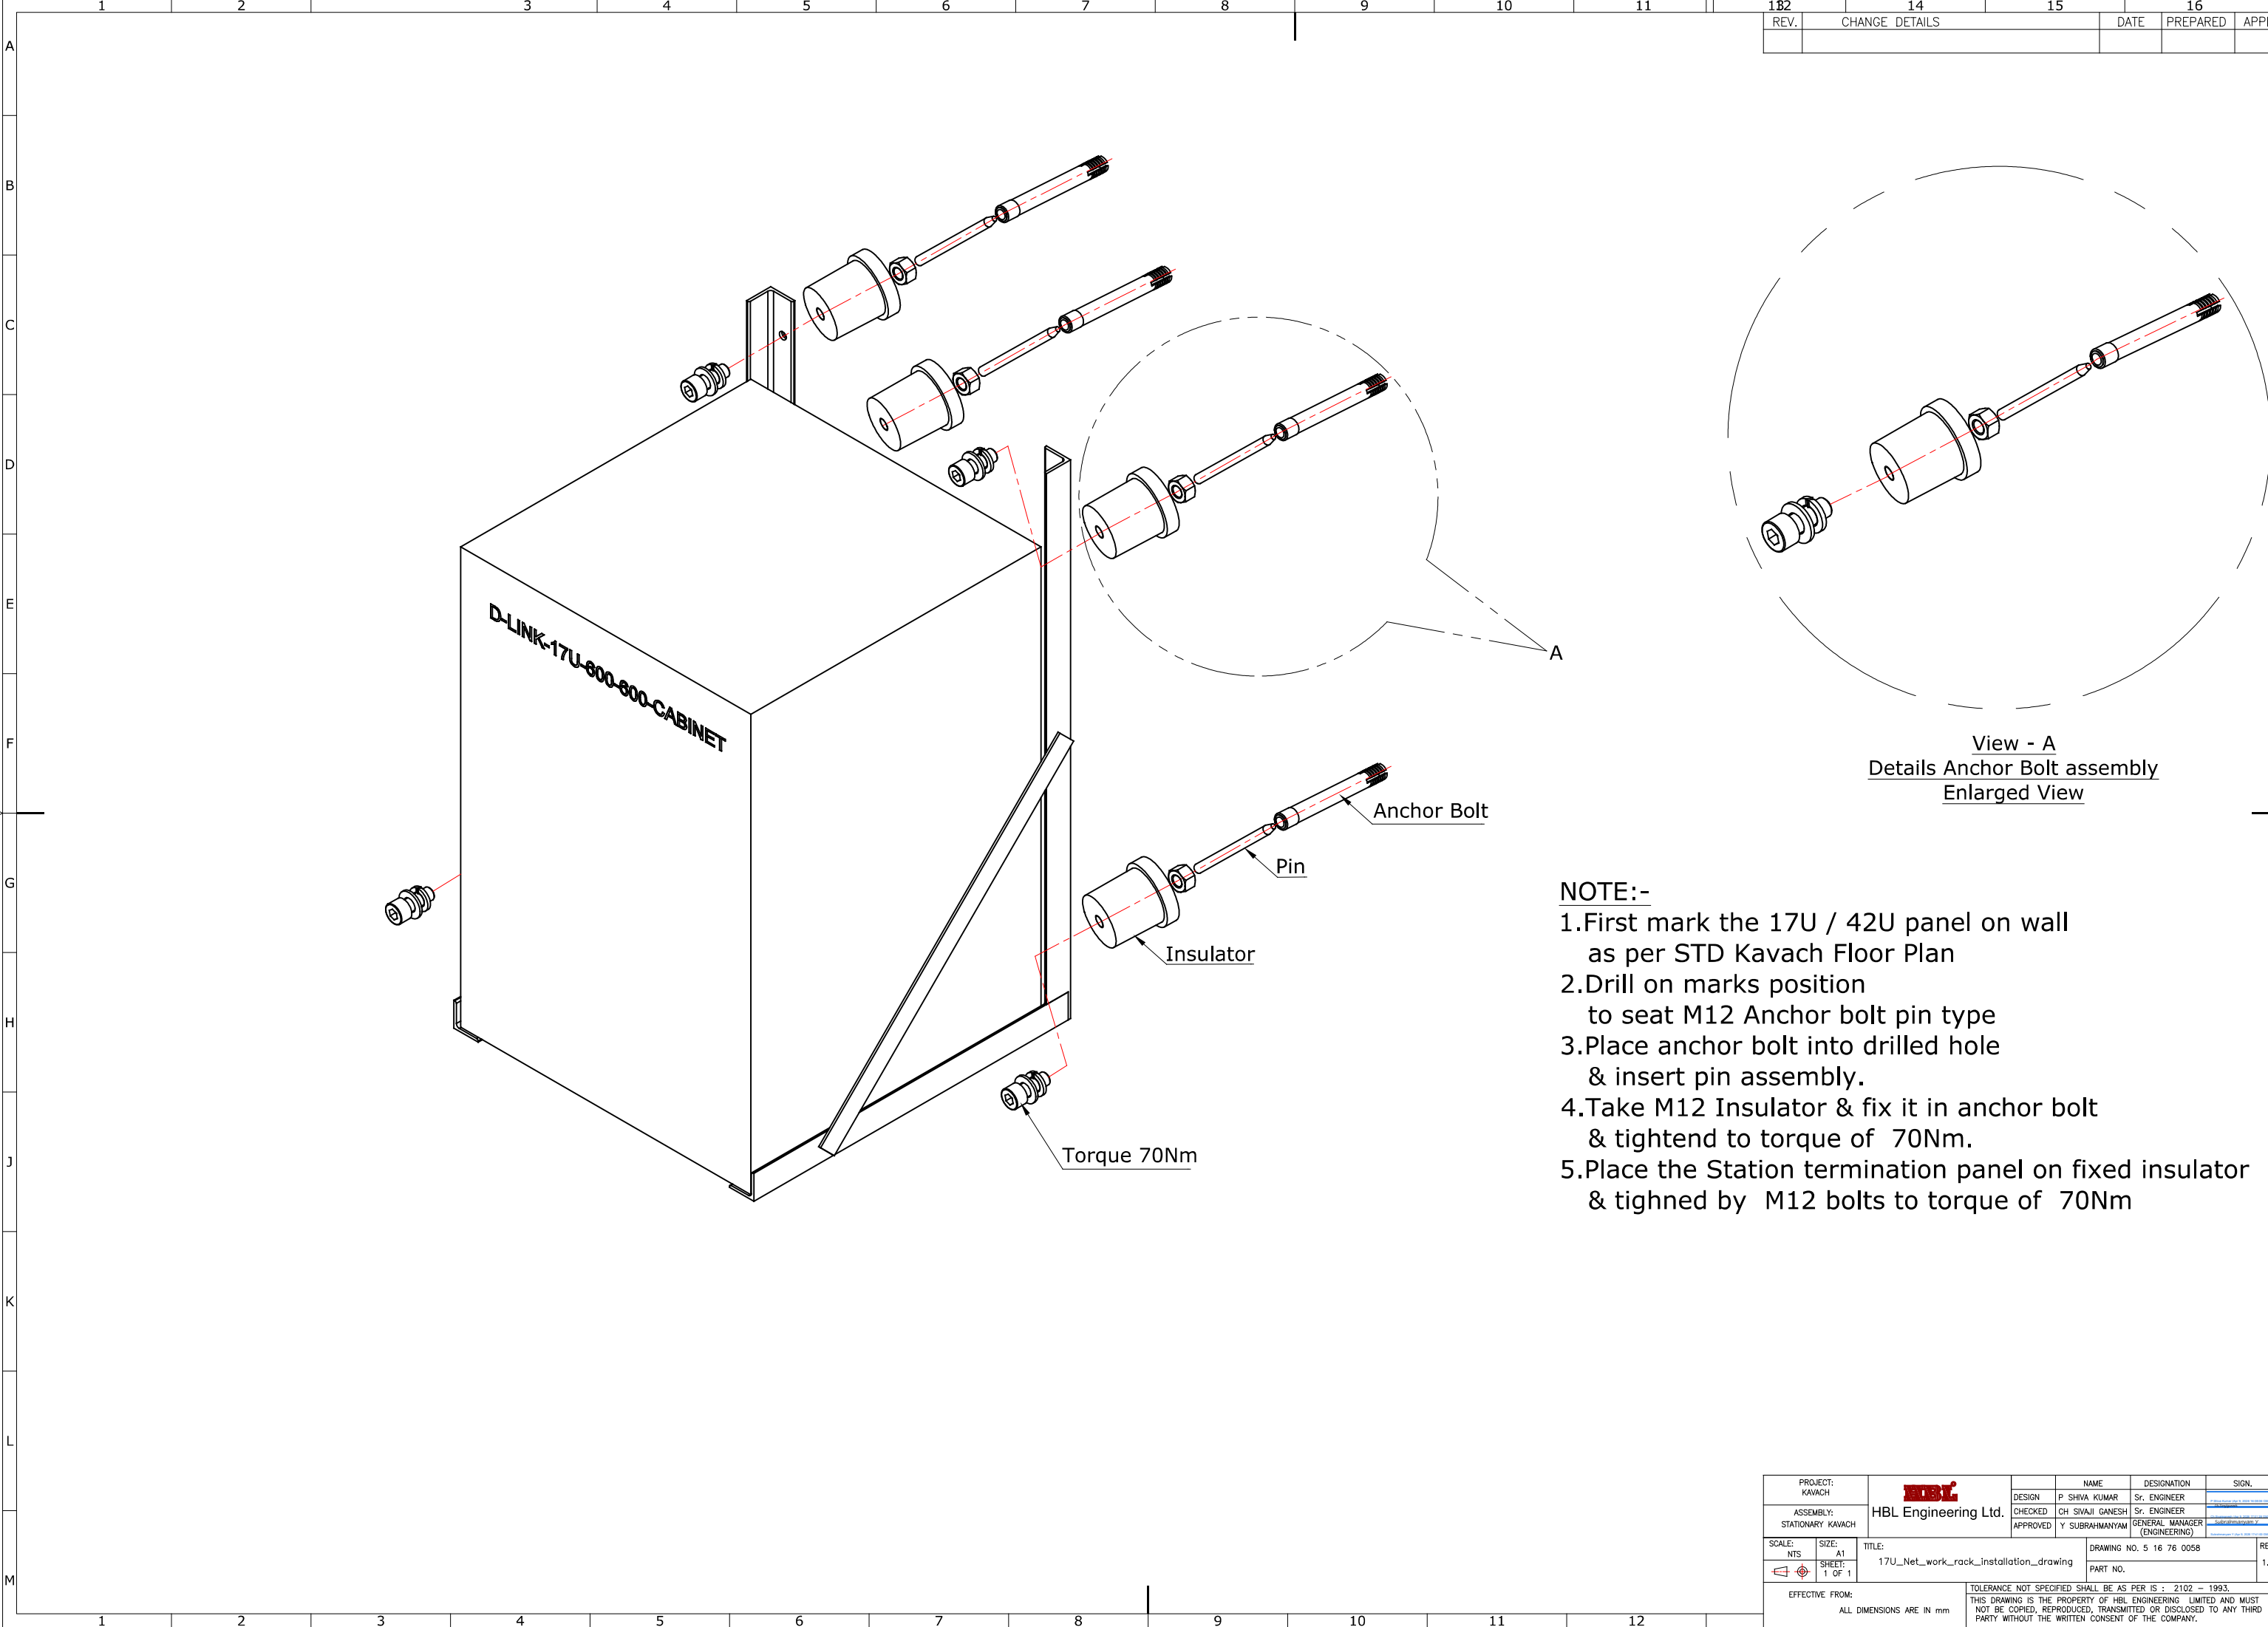

182	14	15	16
REV.	CHANGE DETAILS	DATE	PREPARED APPD.

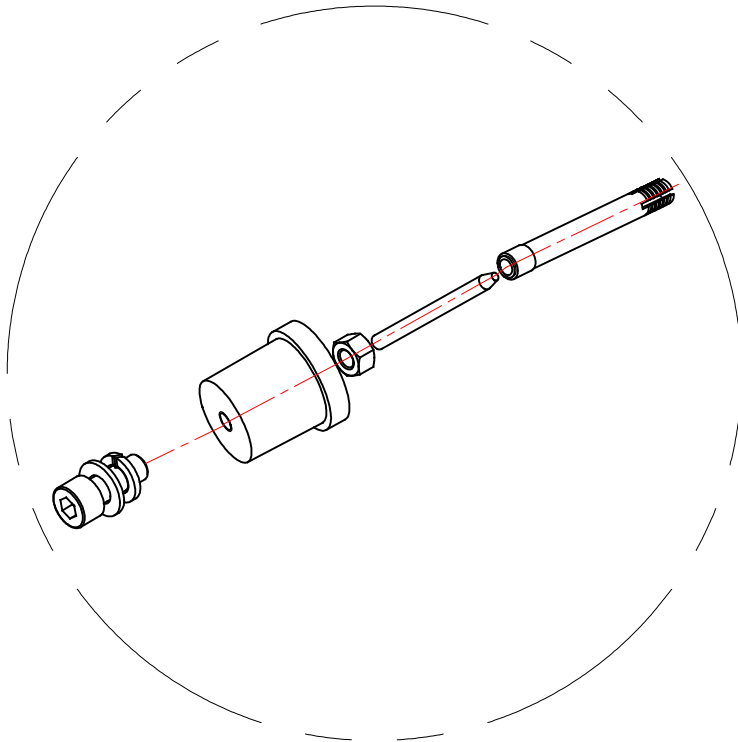

View - A
Details Anchor Bolt assembly
Enlarged View

- NOTE:-
- 1.First mark the 17U / 42U panel on wall as per STD Kavach Floor Plan
 - 2.Drill on marks position to seat M12 Anchor bolt pin type
 - 3.Place anchor bolt into drilled hole & insert pin assembly.
 - 4.Take M12 Insulator & fix it in anchor bolt & tightend to torque of 70Nm.
 - 5.Place the Station termination panel on fixed insulator & tighned by M12 bolts to torque of 70Nm

PROJECT: KAVACH	HBL	NAME	DESIGNATION	SIGN.
ASSEMBLY: STATIONARY KAVACH	HBL Engineering Ltd.	DESIGN P. SHIVA KUMAR Sr. ENGINEER	Sr. ENGINEER	
		CHECKED CH SIVAJI GANESH Sr. ENGINEER	Sr. ENGINEER	
		APPROVED Y SUBRAHMANYAM GENERAL MANAGER (ENGINEERING)		
SCALE: NTS	SIZE: A1 SHEET: 1 OF 1	TITLE: 17U_Net_work_rack_installation_drawing	DRAWING NO. 5 16 76 0058 PART NO.	REV. 1.0
EFFECTIVE FROM: ALL DIMENSIONS ARE IN mm		TOLERANCE NOT SPECIFIED SHALL BE AS PER IS : 2102 - 1993. THIS DRAWING IS THE PROPERTY OF HBL ENGINEERING LIMITED AND MUST NOT BE COPIED, REPRODUCED, TRANSMITTED OR DISCLOSED TO ANY THIRD PARTY WITHOUT THE WRITTEN CONSENT OF THE COMPANY.		

516760058_17U_Net_work_rack_installation_drawing

Final Audit Report

2026-04-09

Created:	2026-04-09 (India Standard Time)
By:	Subrahmanyam Y (subrahmanyam.yadavalli@hbl.in)
Status:	Signed
Transaction ID:	CBJCHBCAABAApk49FdgfoTiBdELdAYamKjDZOBsl5YCR

"516760058_17U_Net_work_rack_installation_drawing" History

-  Document created by Subrahmanyam Y (subrahmanyam.yadavalli@hbl.in)
2026-04-09 - 4:05:20 PM GMT+5.5- IP address: 122.187.81.114
-  Document emailed to P Shiva Kumar (shivakumar.pudhoju@hbl.in) for signature
2026-04-09 - 4:06:40 PM GMT+5.5
-  Email viewed by P Shiva Kumar (shivakumar.pudhoju@hbl.in)
2026-04-09 - 4:07:32 PM GMT+5.5- IP address: 122.187.81.114
-  Document e-signed by P Shiva Kumar (shivakumar.pudhoju@hbl.in)
Signature Date: 2026-04-09 - 4:08:06 PM GMT+5.5 - Time Source: server- IP address: 122.187.81.114
-  Document emailed to sivajiganesh.chennuboyina@hbl.in for signature
2026-04-09 - 4:08:08 PM GMT+5.5
-  Email viewed by sivajiganesh.chennuboyina@hbl.in
2026-04-09 - 5:00:46 PM GMT+5.5- IP address: 122.187.81.114
-  Signer sivajiganesh.chennuboyina@hbl.in entered name at signing as Ch.Sivajiganesh
2026-04-09 - 5:01:26 PM GMT+5.5- IP address: 122.187.81.114
-  Document e-signed by Ch.Sivajiganesh (sivajiganesh.chennuboyina@hbl.in)
Signature Date: 2026-04-09 - 5:01:28 PM GMT+5.5 - Time Source: server- IP address: 122.187.81.114
-  Document emailed to Subrahmanyam Y (subrahmanyam.yadavalli@hbl.in) for signature
2026-04-09 - 5:01:30 PM GMT+5.5
-  Email viewed by Subrahmanyam Y (subrahmanyam.yadavalli@hbl.in)
2026-04-09 - 5:40:31 PM GMT+5.5- IP address: 122.187.81.114



Document e-signed by Subrahmanyam Y (subrahmanyam.yadavalli@hbl.in)

Signature Date: 2026-04-09 - 5:41:00 PM GMT+5.5 - Time Source: server- IP address: 122.187.81.114



Agreement completed.

2026-04-09 - 5:41:00 PM GMT+5.5