




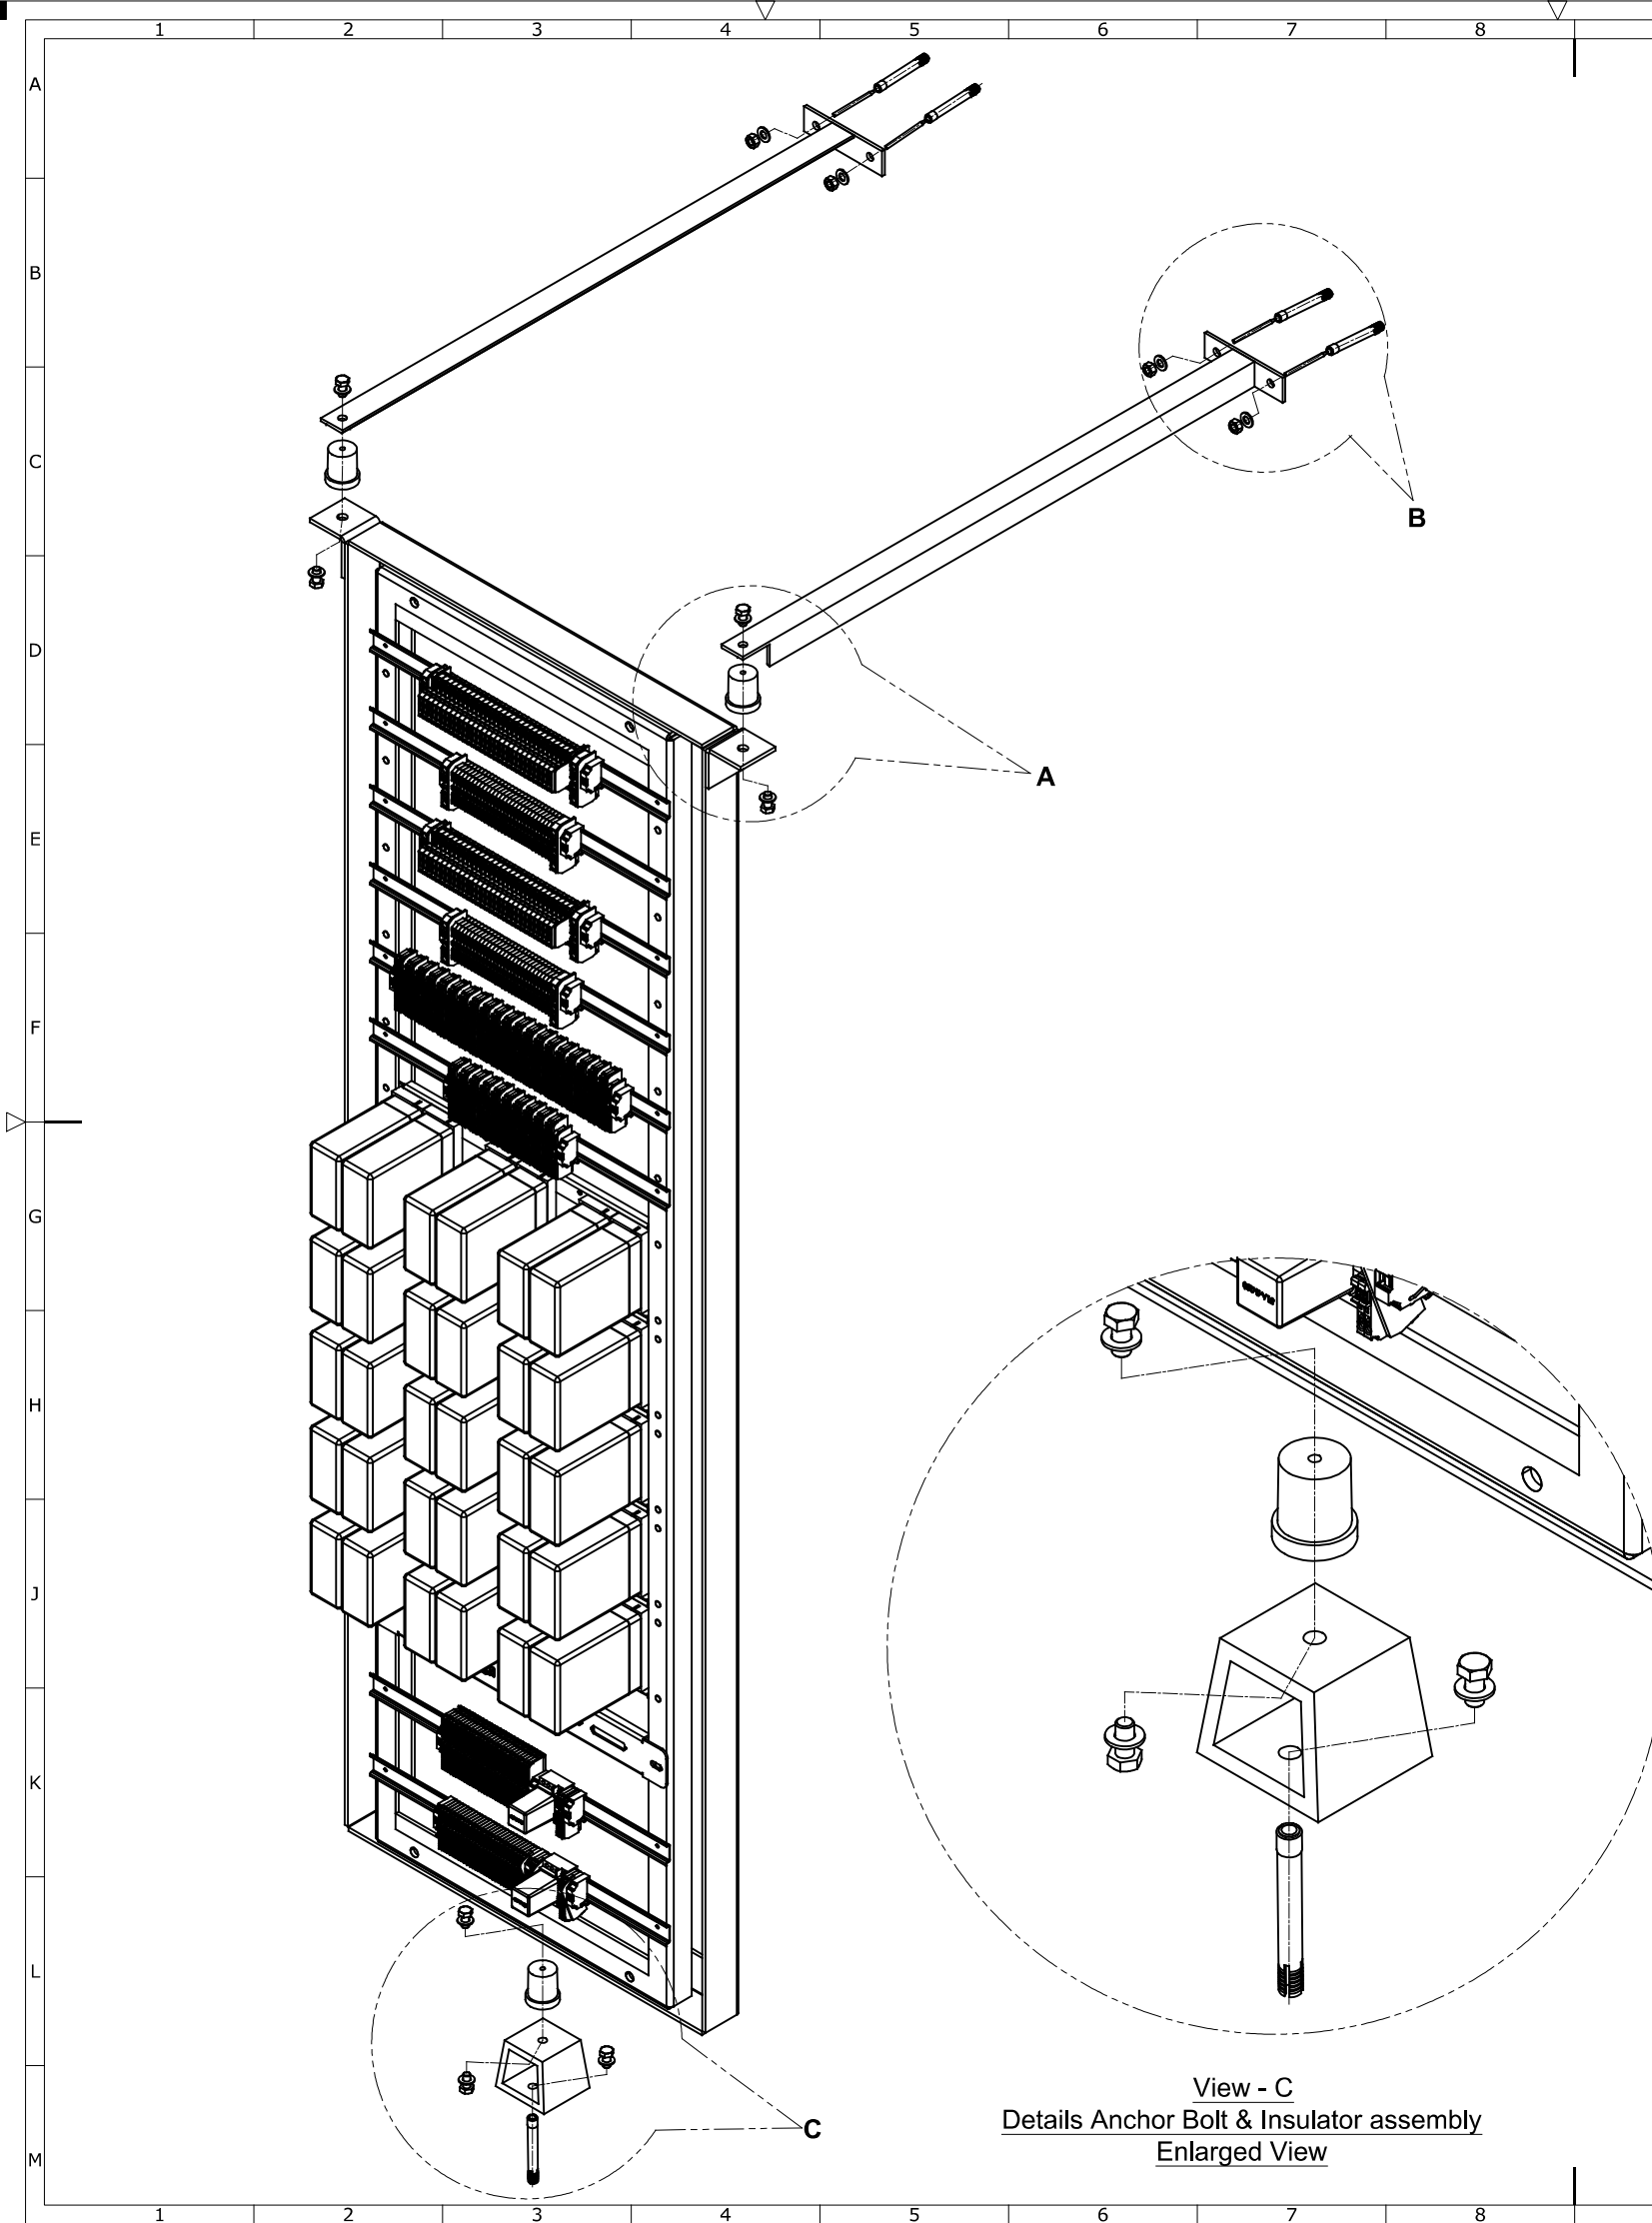

13		14		15		16	
REV.	CHANGE DETAILS	DATE	PREPARED	APPD.			

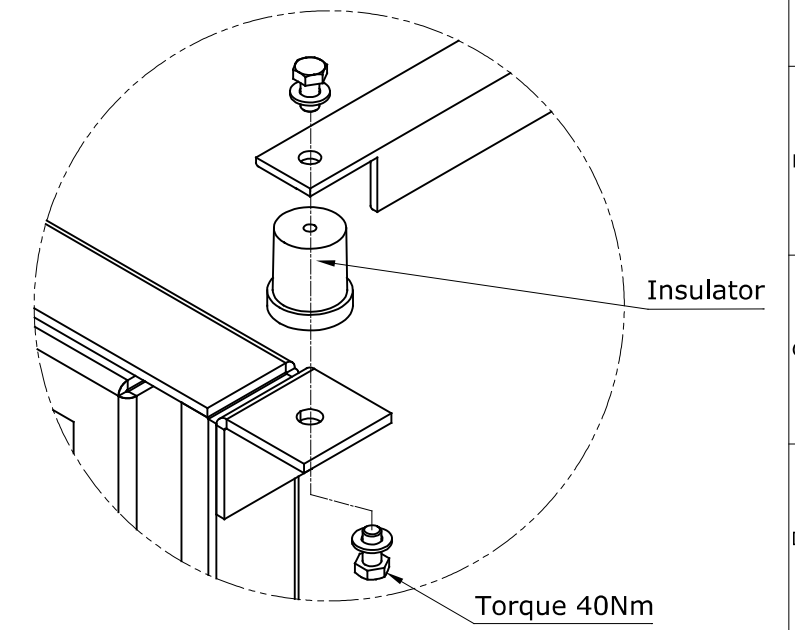

View - A
Details Anchor Bolt assembly
Enlarged View

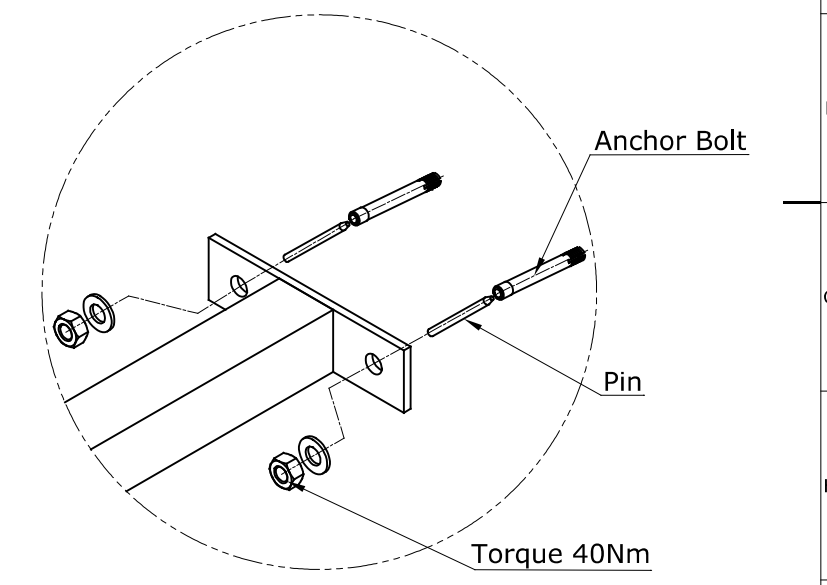

View - B
Details Angle Bracket assembly
Enlarged View

- NOTE:-**
- 1.First mark the Relay Rack stand on wall & floor as per STD Kavach Floor Plan
 - 2.Drill on marked position to seat M10 Anchor bolt pin type
 - 3.Place anchor bolt into drilled hole & insert pin assembly.
 - 4.Take M10 Insulator & fix it in anchor bolt & tightend to torque of 40Nm.
 - 5.Place the Relay Rack on fixed insulator & tighned by M10 bolts to torque of 40Nm

PROJECT: KAVACH		HBL Engineering Ltd.		NAME P. SHIVA KUMAR	DESIGNATION Sr. ENGINEER	SIGN.
ASSEMBLY: STATIONARY KAVACH		DESIGN CH SIVAJI GANESH		CHECKED Y SUBRAHMANYAM	Sr. ENGINEER	
SCALE: NTS		TITLE: Relay_Rack_Installation_Drawing ASSEMBLY DRAWING INSTRUCTIONS		DRAWING NO. 5 16 76 0059		REV. 1.0
SHEET: 1 OF 1		PART NO.		TOLERANCE NOT SPECIFIED SHALL BE AS PER IS : 2102 - 1993.		
EFFECTIVE FROM:		ALL DIMENSIONS ARE IN mm		THIS DRAWING IS THE PROPERTY OF HBL ENGINEERING LIMITED AND MUST NOT BE COPIED, REPRODUCED, TRANSMITTED OR DISCLOSED TO ANY THIRD PARTY WITHOUT THE WRITTEN CONSENT OF THE COMPANY.		

516760059_Relay_Rack_Installation_Drawing

Final Audit Report

2026-04-20

Created:	2026-04-20 (India Standard Time)
By:	Subrahmanyam Y (subrahmanyam.yadavalli@hbl.in)
Status:	Signed
Transaction ID:	CBJCHBCAABAApQmA9WcA1cZ7fz_5hP1pN_b7428g1Fu5

"516760059_Relay_Rack_Installation_Drawing" History

-  Document created by Subrahmanyam Y (subrahmanyam.yadavalli@hbl.in)
2026-04-20 - 9:07:18 AM GMT+5.5- IP address: 122.187.81.114
-  Document emailed to P Shiva Kumar (shivakumar.pudhoju@hbl.in) for signature
2026-04-20 - 9:09:33 AM GMT+5.5
-  Email viewed by P Shiva Kumar (shivakumar.pudhoju@hbl.in)
2026-04-20 - 9:11:14 AM GMT+5.5- IP address: 122.187.81.114
-  Document e-signed by P Shiva Kumar (shivakumar.pudhoju@hbl.in)
Signature Date: 2026-04-20 - 9:11:46 AM GMT+5.5 - Time Source: server- IP address: 122.187.81.114
-  Document emailed to sivajiganesh.chennuboyina@hbl.in for signature
2026-04-20 - 9:11:48 AM GMT+5.5
-  Email viewed by sivajiganesh.chennuboyina@hbl.in
2026-04-20 - 9:28:24 AM GMT+5.5- IP address: 122.187.81.114
-  Signer sivajiganesh.chennuboyina@hbl.in entered name at signing as Ch.Slvajiganesh
2026-04-20 - 9:30:02 AM GMT+5.5- IP address: 122.187.81.114
-  Document e-signed by Ch.Slvajiganesh (sivajiganesh.chennuboyina@hbl.in)
Signature Date: 2026-04-20 - 9:30:04 AM GMT+5.5 - Time Source: server- IP address: 122.187.81.114
-  Document emailed to Subrahmanyam Y (subrahmanyam.yadavalli@hbl.in) for signature
2026-04-20 - 9:30:06 AM GMT+5.5
-  Email viewed by Subrahmanyam Y (subrahmanyam.yadavalli@hbl.in)
2026-04-20 - 12:58:20 PM GMT+5.5- IP address: 122.187.81.114
-  Document e-signed by Subrahmanyam Y (subrahmanyam.yadavalli@hbl.in)
Signature Date: 2026-04-20 - 12:59:10 PM GMT+5.5 - Time Source: server- IP address: 122.187.81.114

✔ Agreement completed.

2026-04-20 - 12:59:10 PM GMT+5.5